


bauseitige
Lieferung

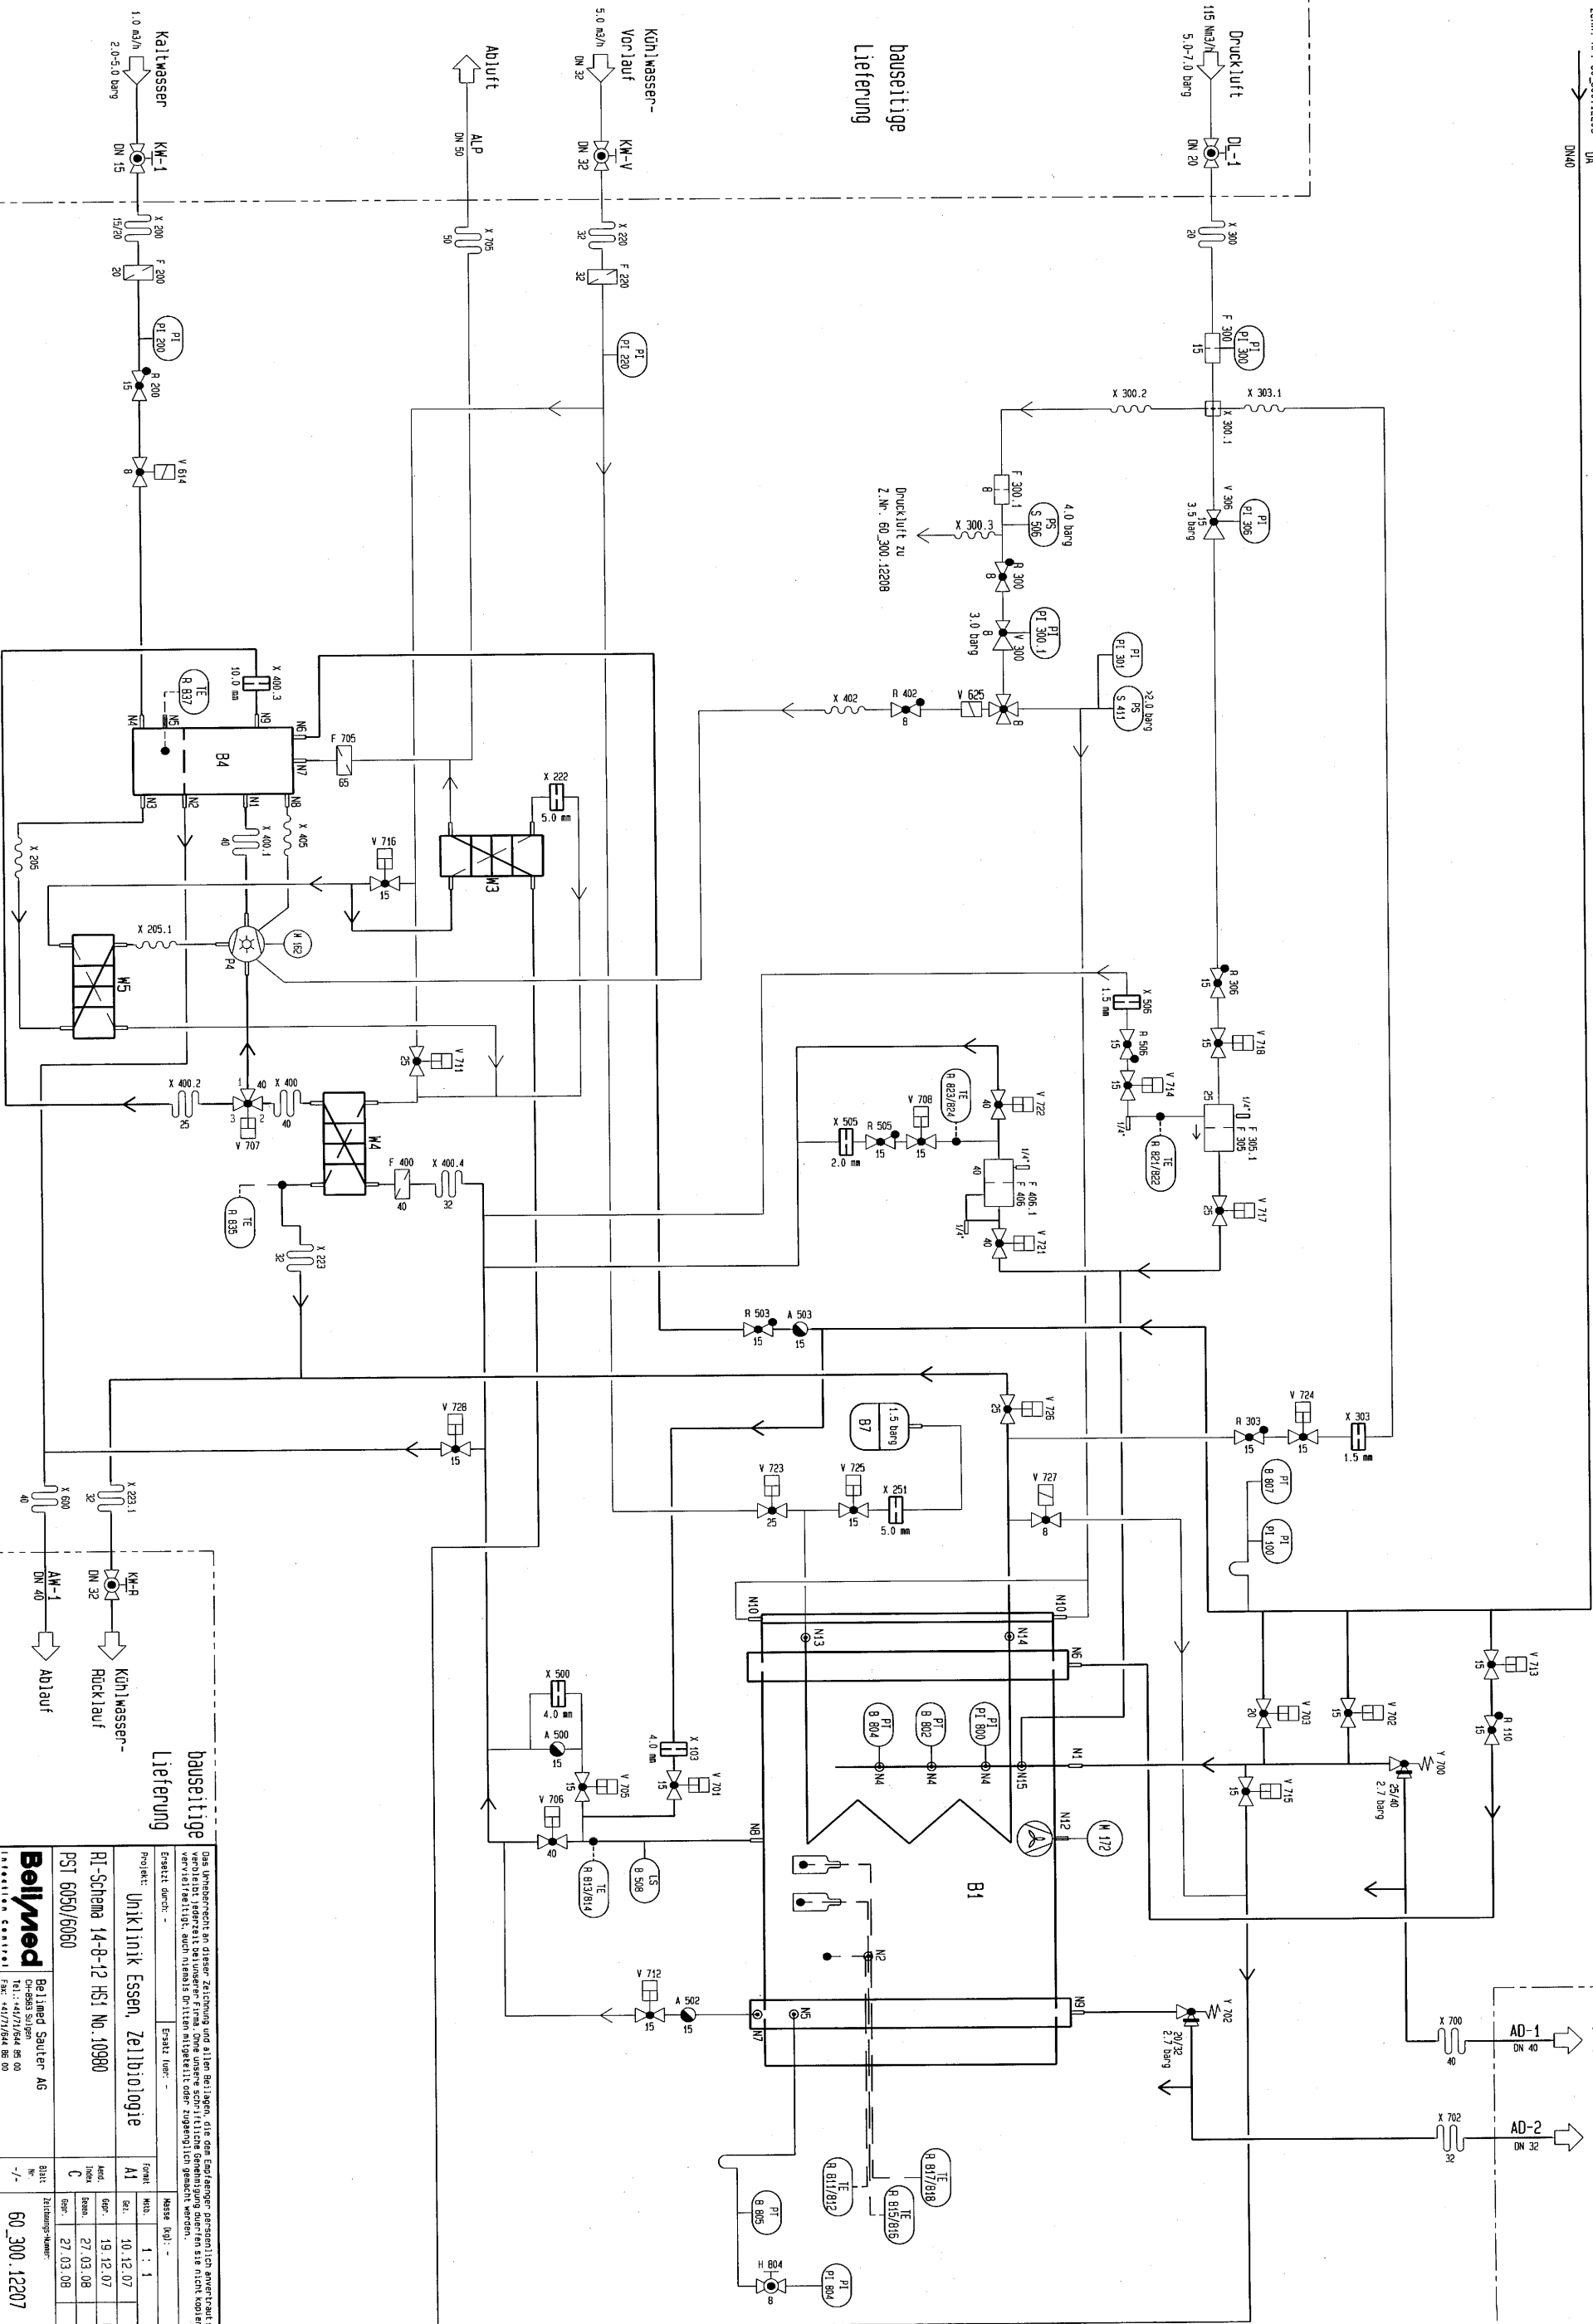

bauseitige
Lieferung

Das Urheberrecht an dieser Zeichnung und allen Beilagen, die den Empfänger persönlich anvertraut sind, verbleibt jederzeit bei unserer Firma. Eine andere schriftliche Genehmigung dürfen Sie nicht kopieren oder verbreiten. Bei Verstoß gegen dieses Verbot wird die Haftung für Schäden übernommen.

Projekt: Uniklinik Essen, Zellbiologie

RI-Schema 14-8-12 HS1 No. 10980

PST 6050/6060

Beilmed Sauter AG

Druck: 10.12.07

Rev.: 19.12.07

Index: 27.03.08

Beitrag: 27.03.08

Zeichnungs-Nr.: 60_300.12207

bauseitige
Lieferung

Abdampf
Kammer

Abdampf
Mantel